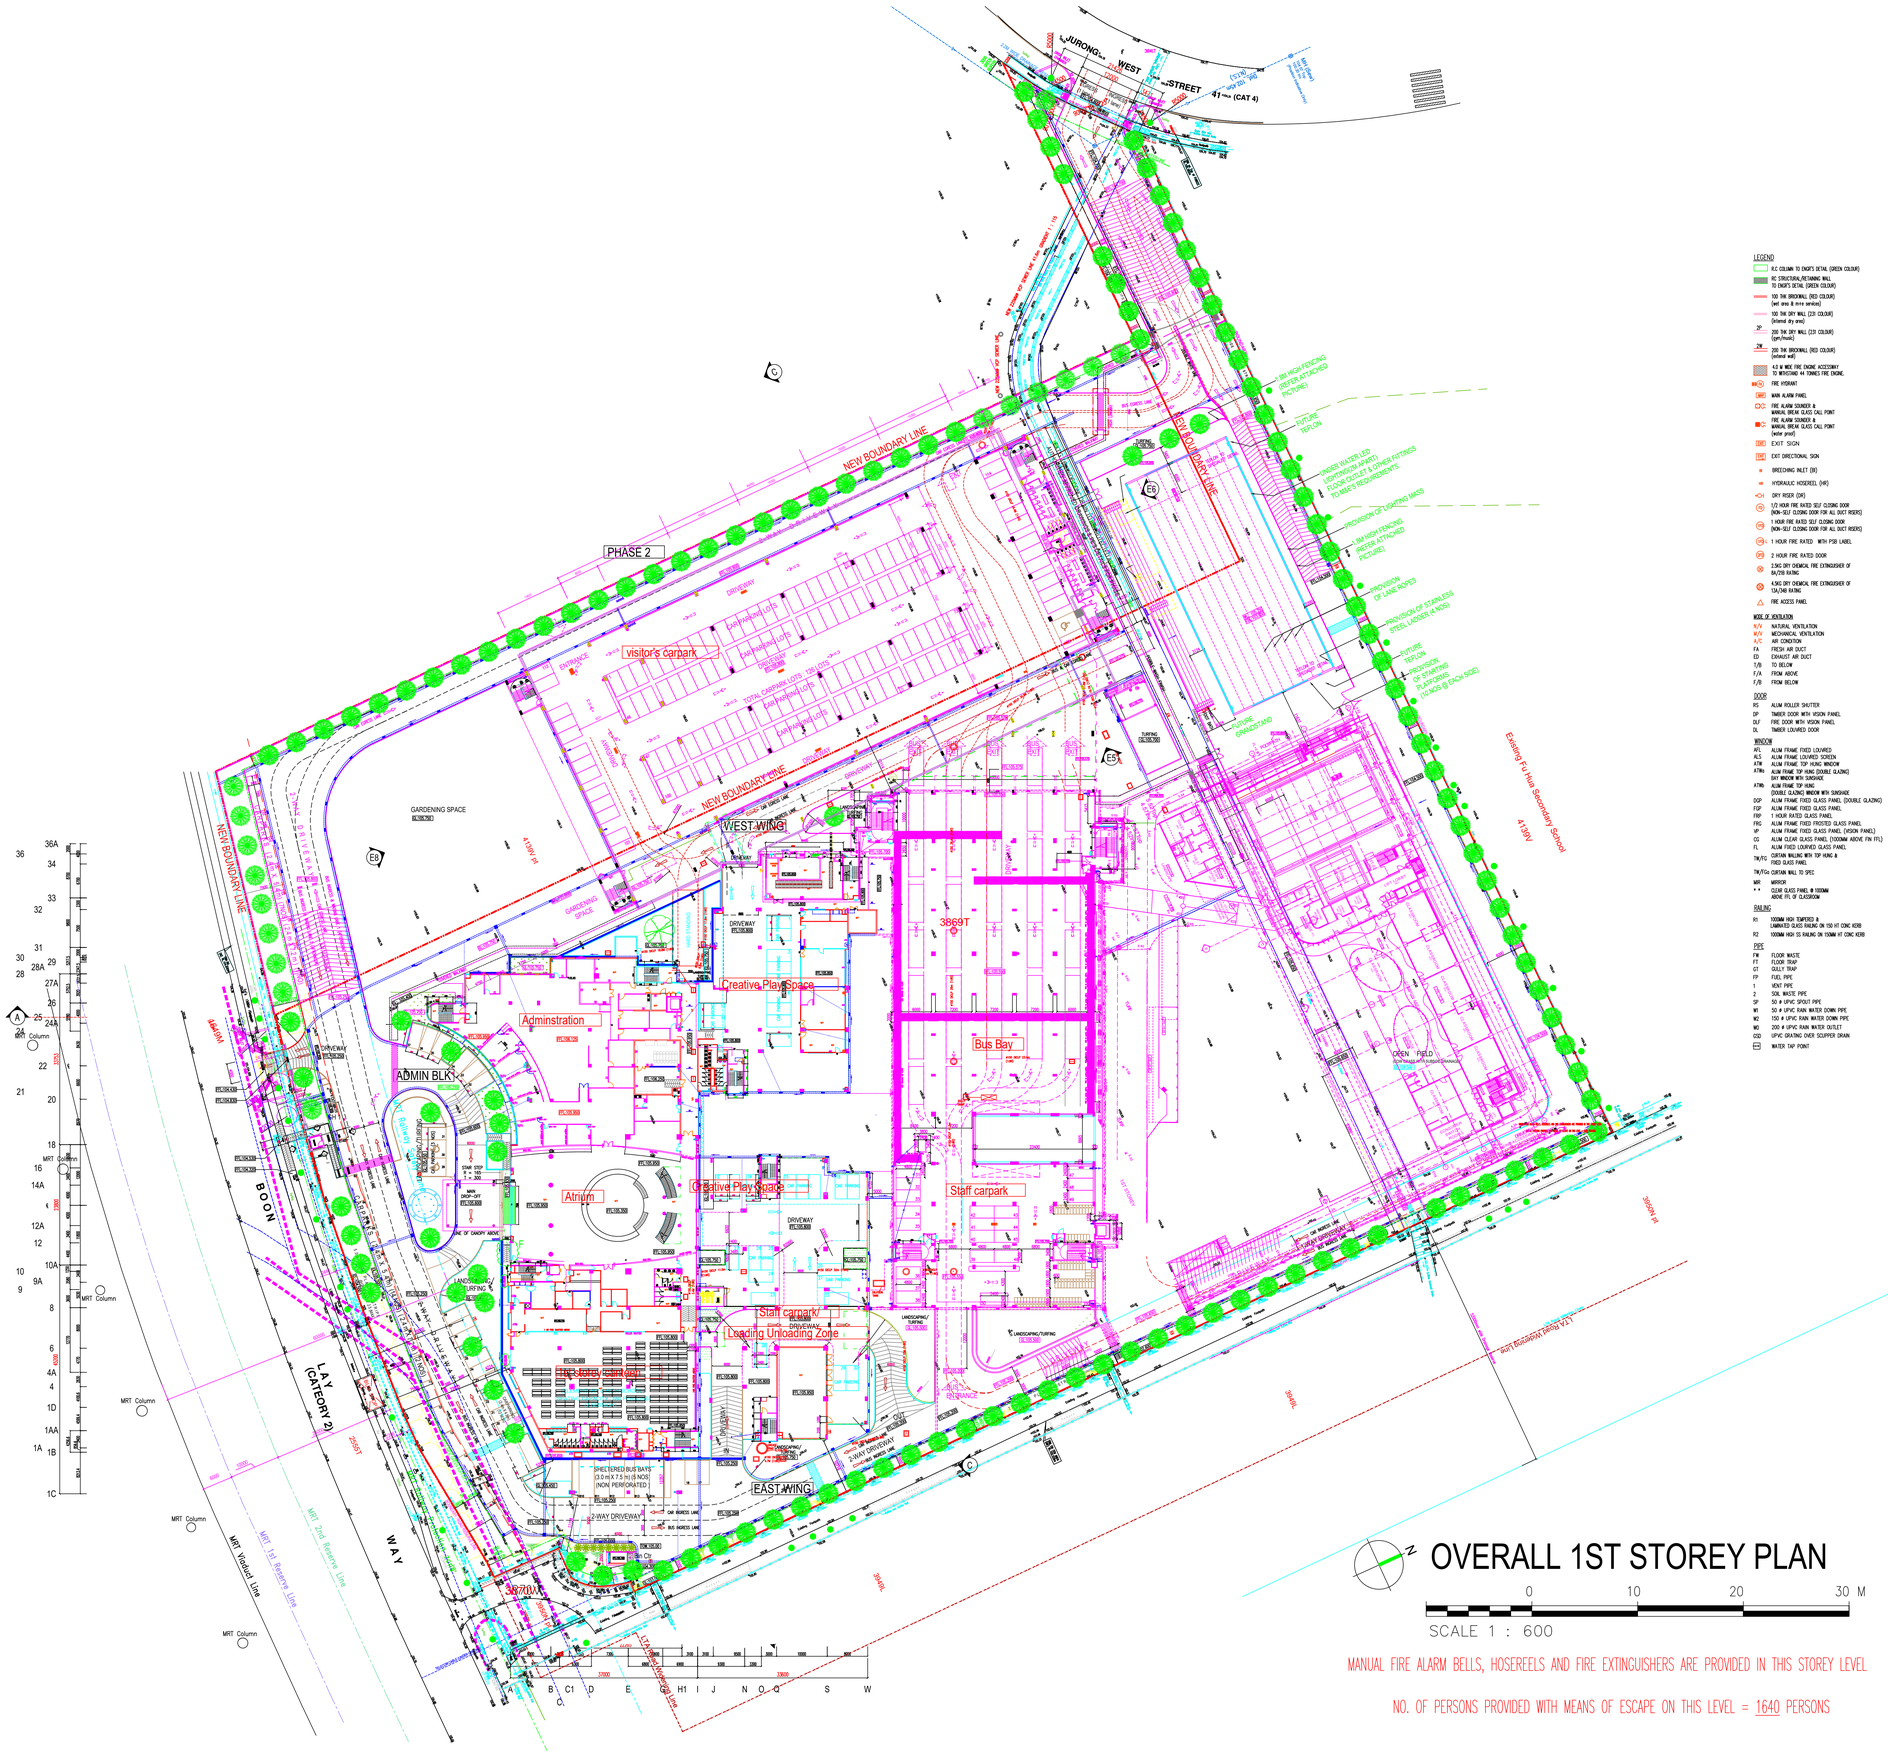

OVERALL 1ST STOREY PLAN

SCALE 1 : 600

0 10 20 30 M

MANUAL FIRE ALARM BELLS, HOSEREELS AND FIRE EXTINGUISHERS ARE PROVIDED IN THIS STOREY LEVEL

NO. OF PERSONS PROVIDED WITH MEANS OF ESCAPE ON THIS LEVEL = 1640 PERSONS

LEGEND

- RC COLUMN TO ENGR'S DETAIL (GREEN COLOUR)
- RC STRUCTURAL/RETAINING WALL TO ENGR'S DETAIL (GREEN COLOUR)
- 100 THK BRICKWALL (RED COLOUR) (wet area & ext walls)
- 100 THK DRY WALL (CIR COLOUR) (internal dry area)
- 200 THK DRY WALL (CIR COLOUR) (ggc/hwall)
- 200 THK BRICKWALL (RED COLOUR) (external wall)
- 4.5 M WIDE FIRE ENGINE ACCESSWAY TO MINIMUM 4M TURNING FIRE ENGINE.
- FIRE HYDRANT
- MFP MAIN ALARM PANEL
- FIRE ALARM SOUNDER & MANUAL BREAK GLASS CALL POINT
- FIRE ALARM SOUNDER & MANUAL BREAK GLASS CALL POINT (water proof)
- EXIT SIGN
- EXIT DIRECTIONAL SIGN
- BREECHING INLET (BI)
- HYDRAULIC HOSEREEL (HR)
- DRY RISER (DR)
- 1/2 HOUR FIRE RATED SELF CLOSING DOOR (NON-SELF CLOSING DOOR FOR ALL DUCT RISERS)
- 1 HOUR FIRE RATED SELF CLOSING DOOR (NON-SELF CLOSING DOOR FOR ALL DUCT RISERS)
- 1 HOUR FIRE RATED WITH FSB LABEL
- 2 HOUR FIRE RATED DOOR
- 2.5KG DRY CHEMICAL FIRE EXTINGUISHER OF 8A/70B RATING
- 4.5KG DRY CHEMICAL FIRE EXTINGUISHER OF 13A/34B RATING
- FIRE ACCESS PANEL

MODE OF VENTILATION

- N/V NATURAL VENTILATION
- M/V MECHANICAL VENTILATION
- A/C AIR CONDITION
- FA FRESH AIR DUCT
- ED EXHAUST AIR DUCT
- T/B TO BELOW
- F/A FROM ABOVE
- F/B FROM BELOW

DOOR

- RS ALUM ROLLER SHUTTER
- DP TIMBER DOOR WITH VISION PANEL
- DLF FIRE DOOR WITH VISION PANEL
- DL TIMBER LOUVRED DOOR

WINDOW

- AVL ALUM FRAME FIXED LOUVRED
- ALS ALUM FRAME LOUVRED SCREEN
- ATW ALUM FRAME TOP HUNG WINDOW
- ATWd ALUM FRAME TOP HUNG DOUBLE GLAZING DAY WINDOW WITH SUNSHADE
- ATWn ALUM FRAME TOP HUNG DOUBLE GLAZING WINDOW WITH SUNSHADE
- DGP ALUM FRAME FIXED GLASS PANEL (DOUBLE GLAZING)
- FGP ALUM FRAME FIXED GLASS PANEL
- FRP 1 HOUR RATED GLASS PANEL
- FRG ALUM FRAME FIXED FROSTED GLASS PANEL
- VP ALUM FRAME FIXED GLASS PANEL (VISION PANEL)
- CG ALUM CLEAR GLASS PANEL (1000MM ABOVE FIN FFL)
- FL ALUM FIXED LOUVRED GLASS PANEL
- TW/FG CURTAIN WALLING WITH TOP HUNG & FIXED GLASS PANEL
- TW/Fgs CURTAIN WALL TO SPEC
- MIR MIRROR
- * * CLEAR GLASS PANEL @ 1000MM ABOVE FFL OF CLASSROOM

RAILING

- R1 1000MM HIGH TEMPERED & LAMINATED GLASS RAILING ON 150 HT CONC KERB
- R2 1000MM HIGH SS RAILING ON 150MM HT CONC KERB

PIPE

- FW FLOOR WASTE
- FT FLOOR TRAP
- GT GULLY TRAP
- FP FUEL PIPE
- 1 VENT PIPE
- 2 SOIL WASTE PIPE
- SP 50 ø UPVC SPOUT PIPE
- W1 50 ø UPVC RAIN WATER DOWN PIPE
- W2 150 ø UPVC RAIN WATER DOWN PIPE
- WO 200 ø UPVC RAIN WATER OUTLET
- GSD UPVC GRATING OVER SCUPPER DRAIN
- WATER TAP POINT

1 sheet of 6

MAJOR PROJECT

BUILDING AND CONSTRUCTION AUTHORITY
APPROVED UNDER SECTION 5/ SECTION 5A OF THE BUILDING CONTROL ACT (CHAPTER 29)

PROJECT REF. NO. : A1166-00088-2007-BP01

FOR COMMISSIONER OF BUILDING CONTROL

APPLICANT:

Zhang Jian
CANADIAN INTERNATIONAL SCHOOL PTE LTD
5 TOH TUCK ROAD
Singapore 569979

PROJECT TITLE:

PROPOSED AMENDMENT TO THE APPROVED ERECTION INVOLVING A 6-STOREY CANADIAN INTERNATIONAL SCHOOL WITH ROOF GARDEN ON LOT 03869T AND NEW INCLUSION OF PART LOT 04139V MK 6 AT JURONG WEST ST 41 / BOON LAY WAY
(JURONG WEST PLANNING AREA)

TENURE OF LAND LEASEHOLD

DRAWING TITLE:

OVERALL 1ST STOREY PLAN

QUALIFIED PERSON / ARCHITECT :

ZHAO YANG

M&Y DESIGN ARCHITECTS PTE LTD
120 Lower Delta Road, Cendex Centre,
#13-07, Singapore 169208

Phone: +65 6970 5788
Email: auth_mydesign@hotmail.com

Construction Builder:

TANG MINGMING

GRD BUILDERS PTE LTD
80 Playfair Road #02-01 Kapo Factory
Building BLK A
Singapore 367998
Phone: +65 90389913
Email: Tangmingming@grd.sg

SCALE	As shown	JOB NO :	
CHECKED BY	TANG	Q01/2024	
DRAWN BY	CHENYAN	DRAWING NO :	REV :
DATE	24-01-2025	BP/FP01	

DO NOT SCALE DRAWING. FIGURE DIMENSIONS ARE TO BE FOLLOWED. THE COPYRIGHT OF THESE DRAWINGS REMAIN WITH THE ARCHITECT. NO PART OF THIS DRAWING MAYBE REPRODUCED IN ANY FORM OR ANY MEANS WITHOUT THE WRITTEN PERMISSION FROM STRATEGIC DESIGN INTERNATIONAL.